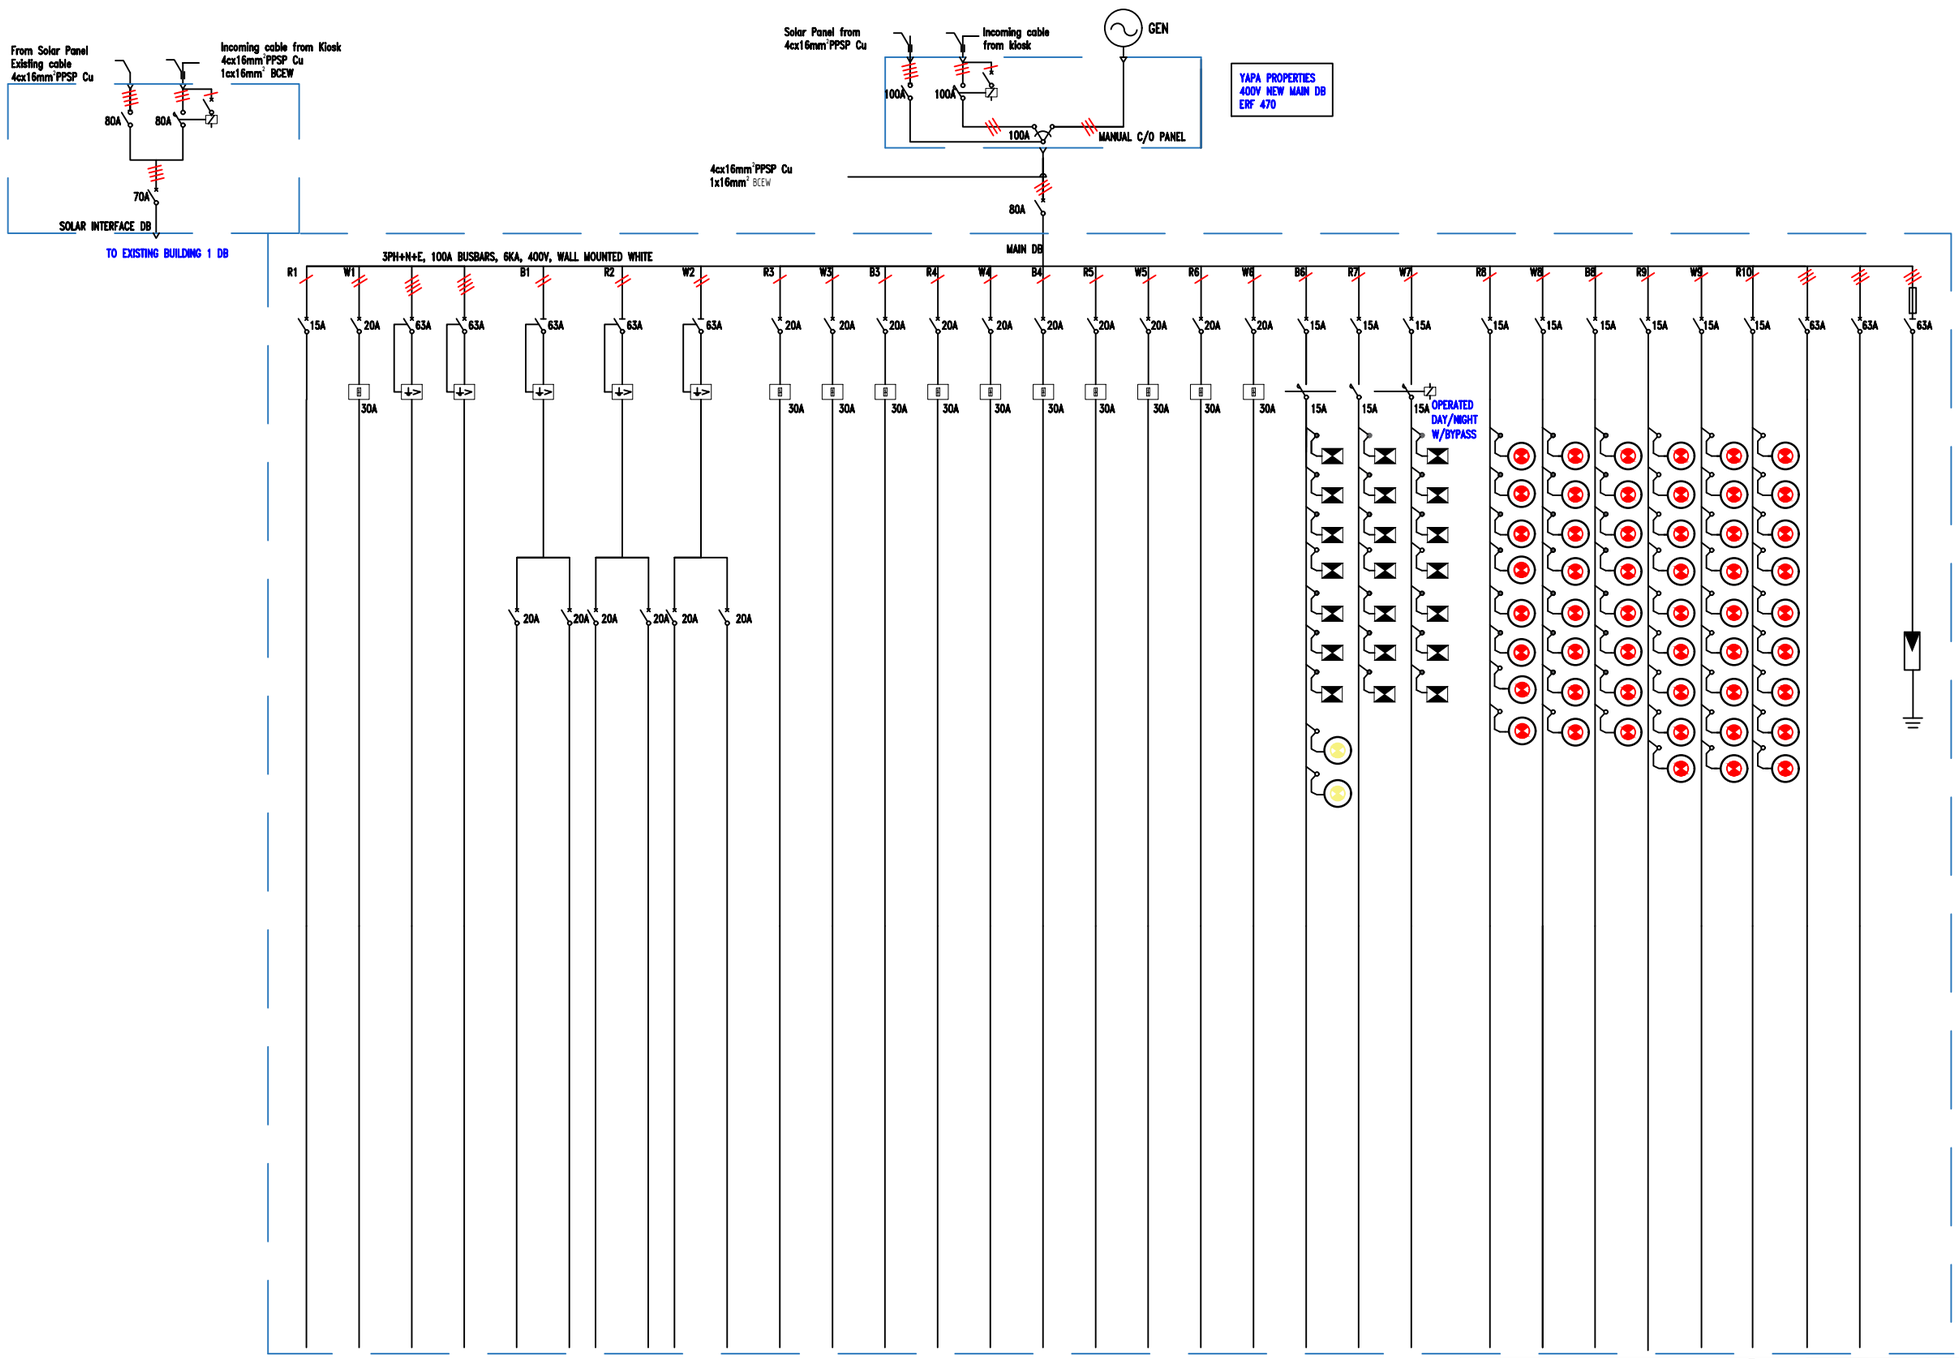


| PHASE | | | | | R-PH | R-PH | W-PH | W-PH | B-PH | B-PH |
|---|---|---|---|---|---|---|---|---|---|---|
| LOAD | | | 28267W | | | | | | | |
| C-SIZE | | | 10mm² | | 4mm² | 2.5mm² | 2.5mm² | | | |
| CIRCT NO | SPARE | SPARE | DBM-P4 | SPARE | DBM-P4 | DBM-P1 | DBM-P2 | SPARE | SPARE | SPARE |
| DESCRIP | | | BATTERY CHARGER | | BATTERY CHARGER | PLUGS | PLUGS | | | |
| QTY | | | 4 | | 2 | 1 | 2 | | | |

| DOUBLE POLE ISOLATOR |
|---|
| 30A |
| 2.5mm² |
| ROLLER DOORS ISOLATOR 1-10 |
| |
| 10 |

| R-PH | W-PH | B-PH | R-PH | W-PH | B-PH | R-PH | W-PH | R-PH | 3PH+N+E | 3PH+N+E | 3PH+N+E |
|---|---|---|---|---|---|---|---|---|---|---|---|
| 450W | 350W | 350W | 2000W | 2000W | 2000W | 2000W | 2250W | 2250W | 27.2KW | 27.2KW | |
| 1.5mm² | 1.5mm² | 1.5mm² | 1.5mm² | 1.5mm² | 1.5mm² | 1.5mm² | 1.5mm² | 1.5mm² | 4Cx10mm² 1Cx10mm² | 4Cx10mm² 1Cx10mm² | |
| DBM-L7 | DBM-L8 | DBM-L9 | DBM-L1 | DBM-L2 | DBM-L3 | DBM-L4 | DBM-L5 | DBM-L6 | GF-DB | 1F-DB | 1F-DB |
| EXT/LIGHTS + SIGN | EXT/LIGHTS | EXT/LIGHTS | LIGHTS ZONE1/MEZ | LIGHTS ZONE2/GNF | LIGHTS ZONE3/GNF | LIGHTS ZONE4/GNF | LIGHTS ZONE5/GNF | LIGHTS ZONE5/GNF | FEEDER | FEEDER | SURGEARREST |
| 9 | 7 | 7 | 8 | 8 | 8 | 8 | 9 | 9 | | | 1 |

RA 100-TYP-005

## NOTES:

a) WALL MOUNTED

b) COLOR EXTERIOR:WHITE

c) COLOR INTERIOR: WHITE (CHASSIS ONLY)

d) CABLE ENTRY: BOTTOM

e) BUSBARS

**APPROVED**

11/1/23
MW

INITIAL HERE

REVISIONS

| No | DATE | CHECKED | APPROVED | DESCRIPTION |
|---|---|---|---|---|
| 01 | 15-11-22 | P.D | M.W.S | ISSUED FOR ACCEPTANCE |

| NUMBER | TITLE |
|---|---|
| | |

REFERENCE DRAWINGS

CHONA DRG. No.: 100-D05

CHONA MALANGA
13 LANGENHOVEN STREET, SECUNDA, 2302
P.O.BOX 692, SECUNDA, 2302
Tel: 072 7461080

| | | | |
|---|---|---|---|
| CONTRACT: | | NAME: | MR(Tlou) Salahana Pr. Eng |
| DRAWN BY: | | Pr. Eng. No.: | 20120248 |
| TRACED BY: | HERVE MBIKAYI | SIGNATURE: | |
| | 15-11-2022 | DATE: | 15-11-2022 |

CLIENT: YAPA PROPERTIES ERF 470 TRICHARD

| | | | |
|---|---|---|---|
| SAP PROJECT No.: | | CHECKED BY: | |
| NETWORK ID No.: | | ACCEPTED BY: | |
| CONTRACT: | | DATE: | |

ERF 470 YAPA PROPERTIES
NEW MAIN DB
SINGLE LINE DIAGRAM

STATION WKS DOC. TYPE S

SCALE: N.T.S.

RA 100-TYP-005 REVISION A